


Blad 1 Plattegrond

Trussconstructie 774,4 x 774,4 cm | trussectie 29 cm | binnenmaat 716,4 cm | opening in zijde D

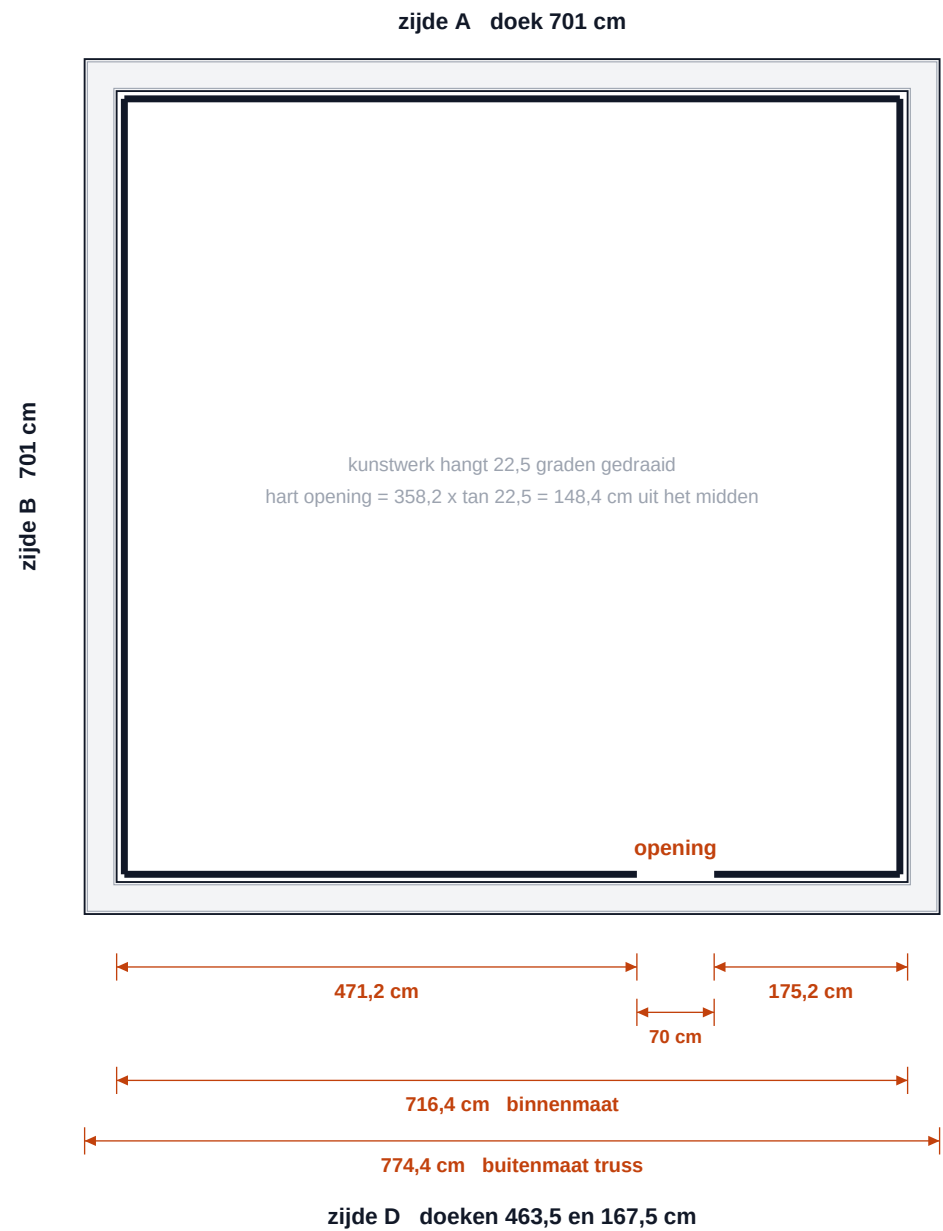

BINNENMATEN

Maat	cm	Hoe
Buitenmaat truss	774,4	opgave trussbouwer
Trussectie	29	standaard 290 mm
Binnenmaat breedte	716,4	774,4 min 2 x 29
Binnenmaat hoogte	321	vloer tot onderkant truss, 350 min 29
Steigerpijp op de vloer	4,8	48,3 mm
Vrije breedte voor het doek	716,4	binnenmaat breedte
Vrije hoogte voor het doek	316,2	boven de pijp, 321 min 4,8
Ruimte spanrubbers opzij	7,7	(716,4 min 701) / 2, naar de staander
Ruimte spanrubbers boven, onder	7,6	(316,2 min 301) / 2, naar de buis
Opening	70	hart 210 uit de hoek, volle hoogte

DOEKEN

Doek	Afgewerkt	Knipmaat	Aantal
A, B, C	701 x 301	715 x 315	3
D-rechts	463,5 x 301	483,5 x 315	1
D-links	167,5 x 301	187,5 x 315	1

Blad 2 Doek A, B en C

Dichte zijden | zoom met singelband op alle vier de randen | zeilringen in de band

3 x knippen knipmaat 715 x 315 cm

zeilringen: 15 boven en 15 onder + 7 per zijband (2 band) = 40 per doek

Hart 2,5 cm uit de afgewerkte rand, daarna h.o.h. 50 cm vanaf beide hoeken. Alleen de middelste afstand wijkt af: 46 cm boven en onder, 46 cm opzij. Hoekringen tellen voor beide randen.



Eerst over de hele rol 5 cm van de breedte af, 320 wordt 315. Daarna alleen nog in de lengte knippen.

Zoomdoorsneden op blad 5.


Blad 3 Doek D-rechts

Zijde met opening | zoom met singelband boven, onder en rechts | tunnelzoom aan de openingszijde

1 x knippen knipmaat 483,5 x 315 cm

zeilringen: 10 boven en 10 onder + 7 per zijband (1 band) = 25 per doek

Hart 2,5 cm uit de afgewerkte rand, daarna h.o.h. 50 cm vanaf beide hoeken. Alleen de middelste afstand wijkt af: 47,5 cm boven en onder, 46 cm opzij. Hoekringen tellen voor beide randen.

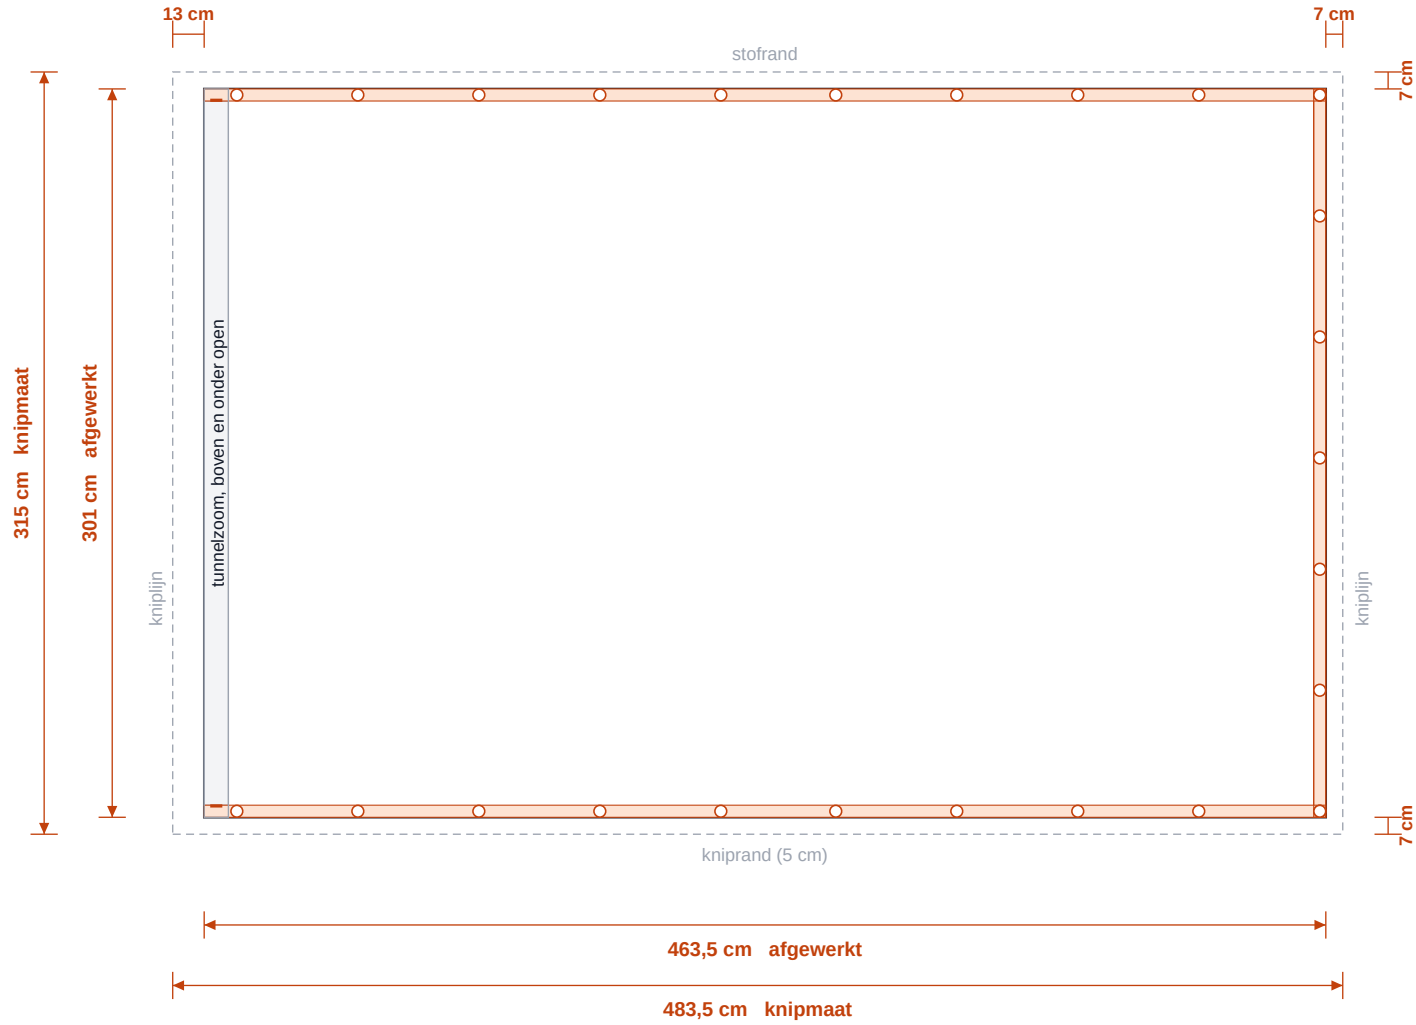

Eerst over de hele rol 5 cm van de breedte af, 320 wordt 315. Daarna alleen nog in de lengte knippen.

Zoomdoorsneden op blad 5.


Blad 4 Doek D-links

Zijde met opening | zoom met singelband boven, onder en links | tunnelzoom aan de openingszijde

1 x knippen knipmaat 187,5 x 315 cm

zeilringen: 4 boven en 4 onder + 7 per zijband (1 band) = 13 per doek

Hart 2,5 cm uit de afgewerkte rand, daarna h.o.h. 50 cm vanaf beide hoeken. Alleen de middelste afstand wijkt af: 51,5 cm boven en onder, 46 cm opzij. Hoekringen tellen voor beide randen.

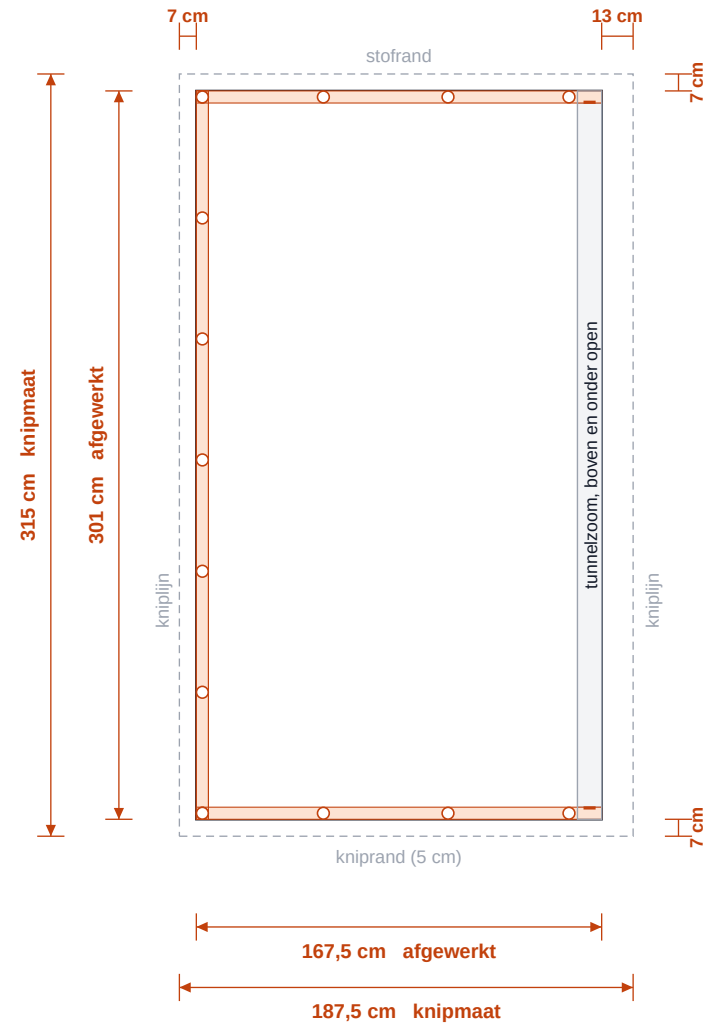

Eerst over de hele rol 5 cm van de breedte af, 320 wordt 315. Daarna alleen nog in de lengte knippen.


Zoomdoorsneden op blad 5.

Blad 5 Zoomdoorsneden

Schaal 1:1 in de breedte | diktes overdreven getekend | stiksel als oranje streeplijn

A Bandzoom


alle randen behalve de verticale randen van de opening | het doek slaat een slag om de band

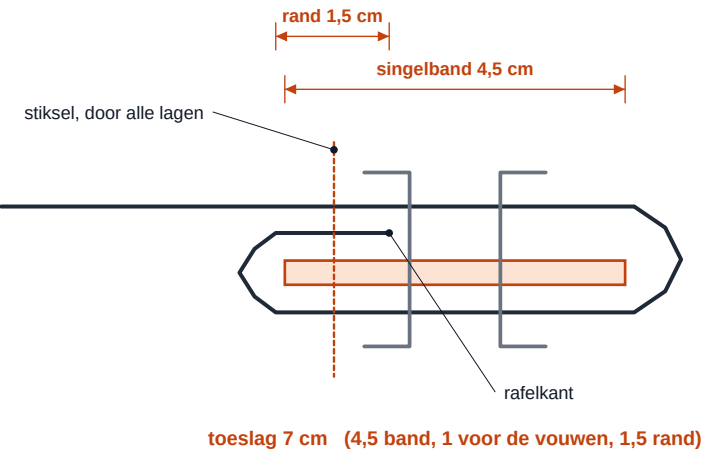

Doorstikken op 1 cm van de binnenvouw, door alle lagen en de band heen. Zeilring 12 mm, hart 2,5 cm uit de afgewerkte rand.

B Tunnelzoom

alleen de verticale randen van de opening, uiteinden blijven open

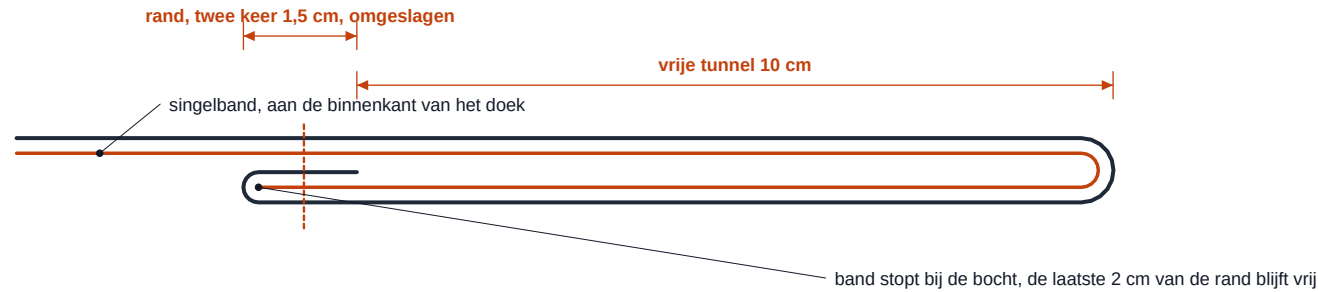


toeslag 13 cm De boven- en onderzoom worden over deze 10 cm niet doorgestikt, anders zit de tunnel dicht.

Breedtes zijn op schaal. De dikte van doek en band is overdreven, anders is de opbouw niet te zien.

Blad 6 Zijaanzicht dichte zijde

zijde A, B en C | een doek van 701 cm over de volle breedte

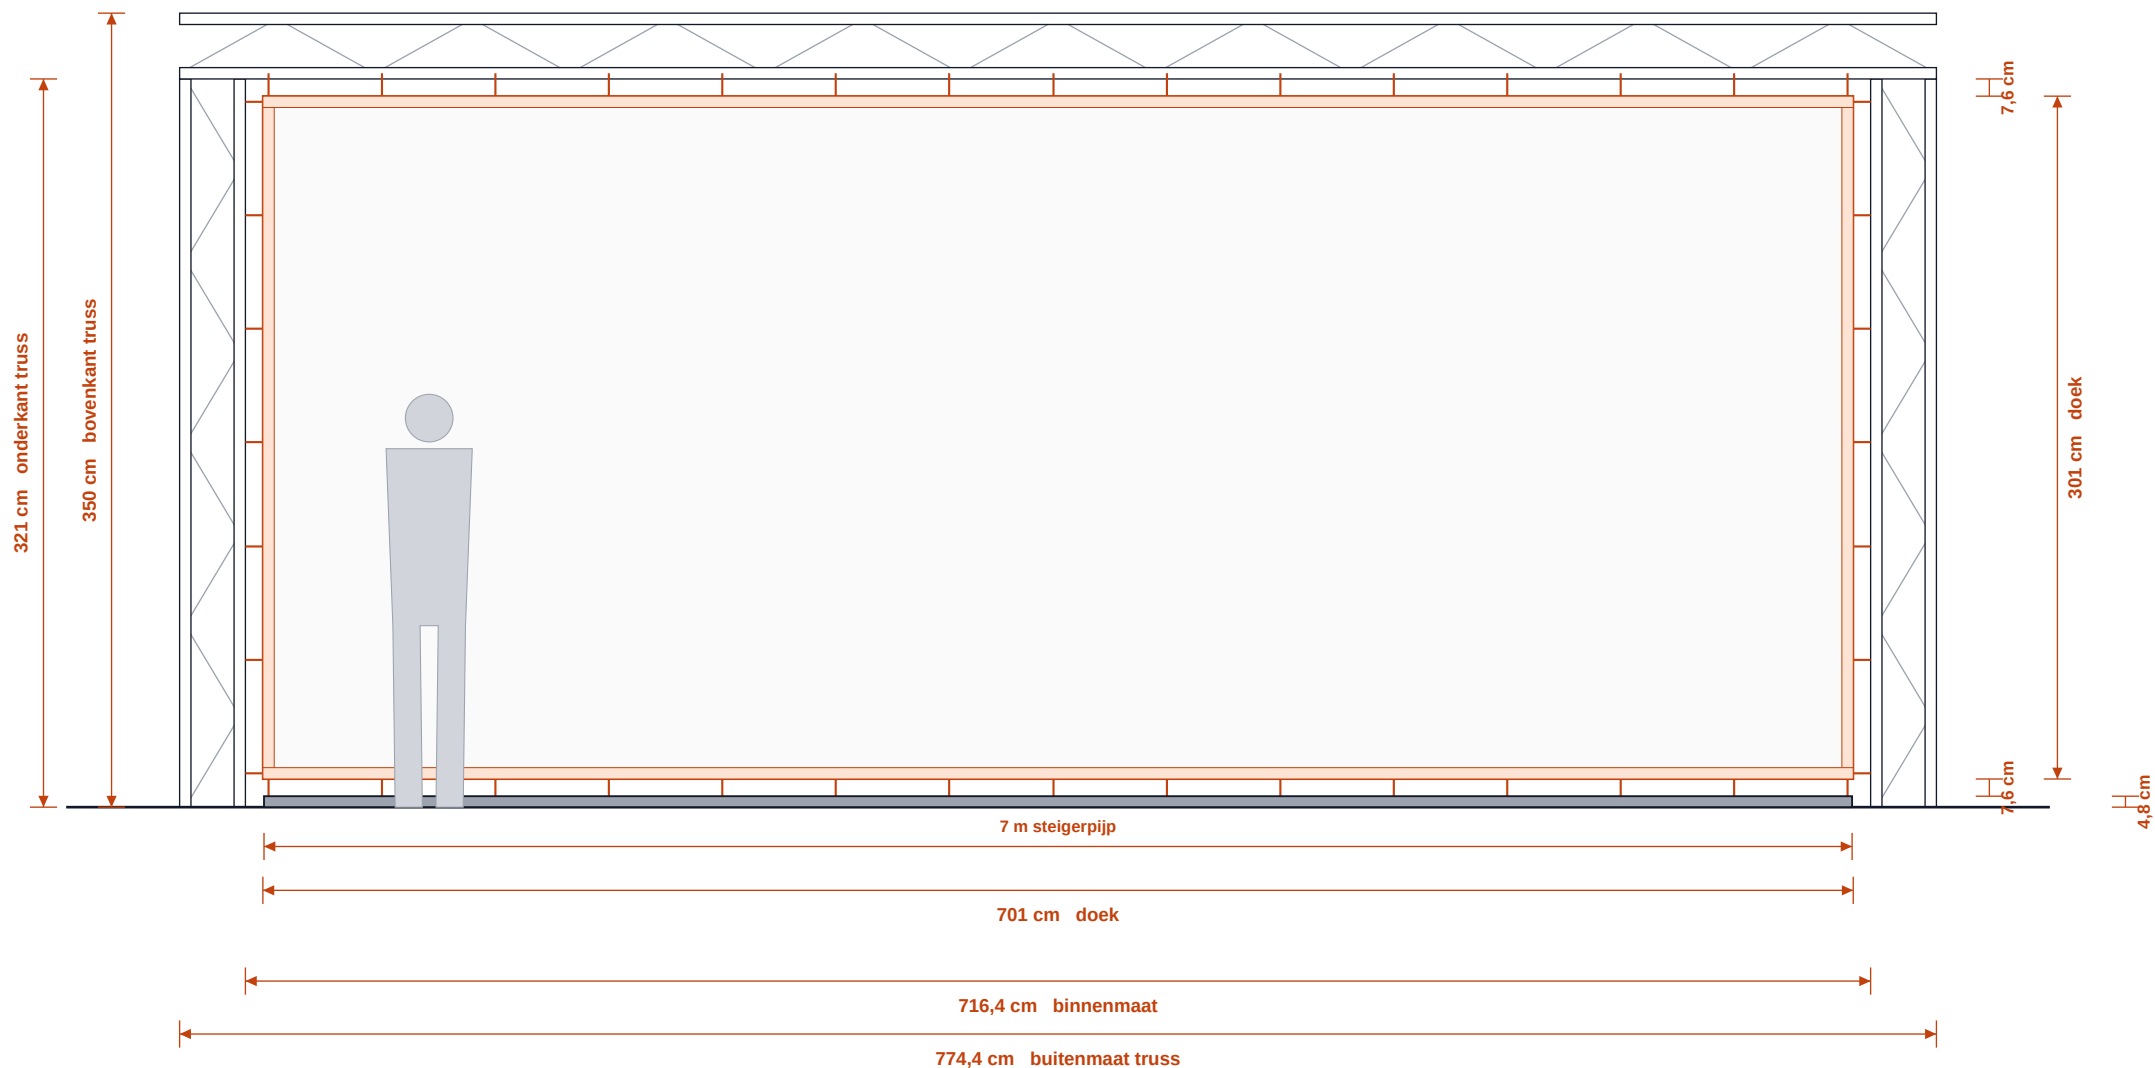


Schaal 1:33. Figuur is 1,80 m.

Boven hangt het doek met spanrubbers aan de onderste buis van de truss. Onder ligt de steigerpijp 48,3 mm op de vloer, spanrubbers eromheen. De opdeling van die 7 m in lengtes is aan de trussbouwer.

De afstand tussen doek en buis is boven en onder gelijk, 7,6 cm. Opzij 7,7 cm naar de staander. Overal spanrubbers met bal van 25 cm. Tiewraps door de zeilringen zijn de terugval als een rand te ruim uitvalt.

Blad 7 Zijaanzicht zijde met opening

zijde D, gezien van binnenuit | doeken van 167,5 en 463,5 cm met een opening van 70 cm

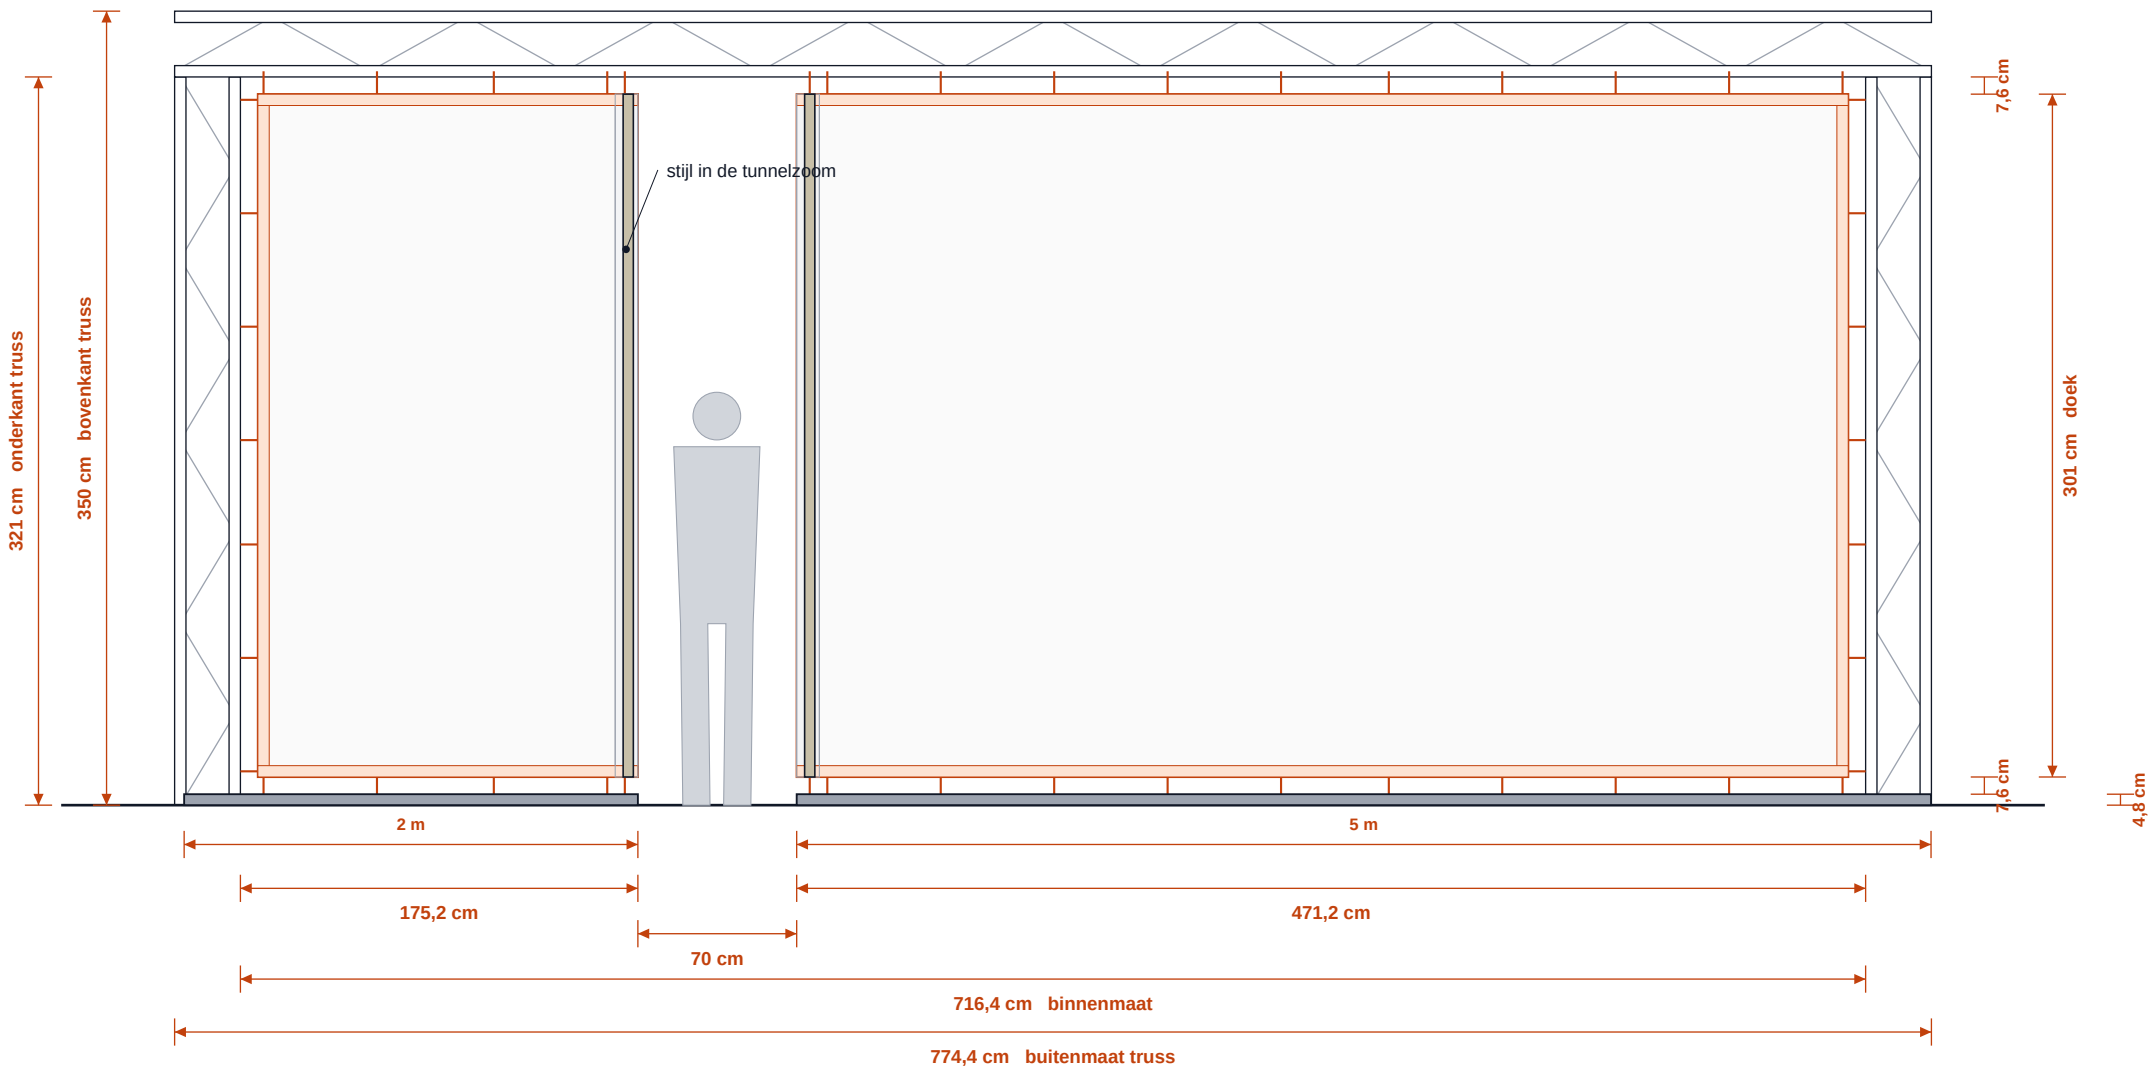

Schaal 1:33. Figuur is 1,80 m.

Boven hangt het doek met spanrubbers aan de onderste buis van de truss. Onder ligt de steigerpijp 48,3 mm op de vloer, spanrubbers eromheen. Bij de opening loopt hij door tot de buitenkant van de staander, zodat 2 en 5 meter passen.

De afstand tussen doek en buis is boven en onder gelijk, 7,6 cm. Opzij 7,7 cm naar de staander. Overal spanrubbers met bal van 25 cm. In de tunnelzoom van de opening komt een stijl van circa 45 mm, keuze en lengte volgen.